
SƠ ĐỒ NHẤT THU TRẠM 110KV CẨM XUYÊN (E18.9)

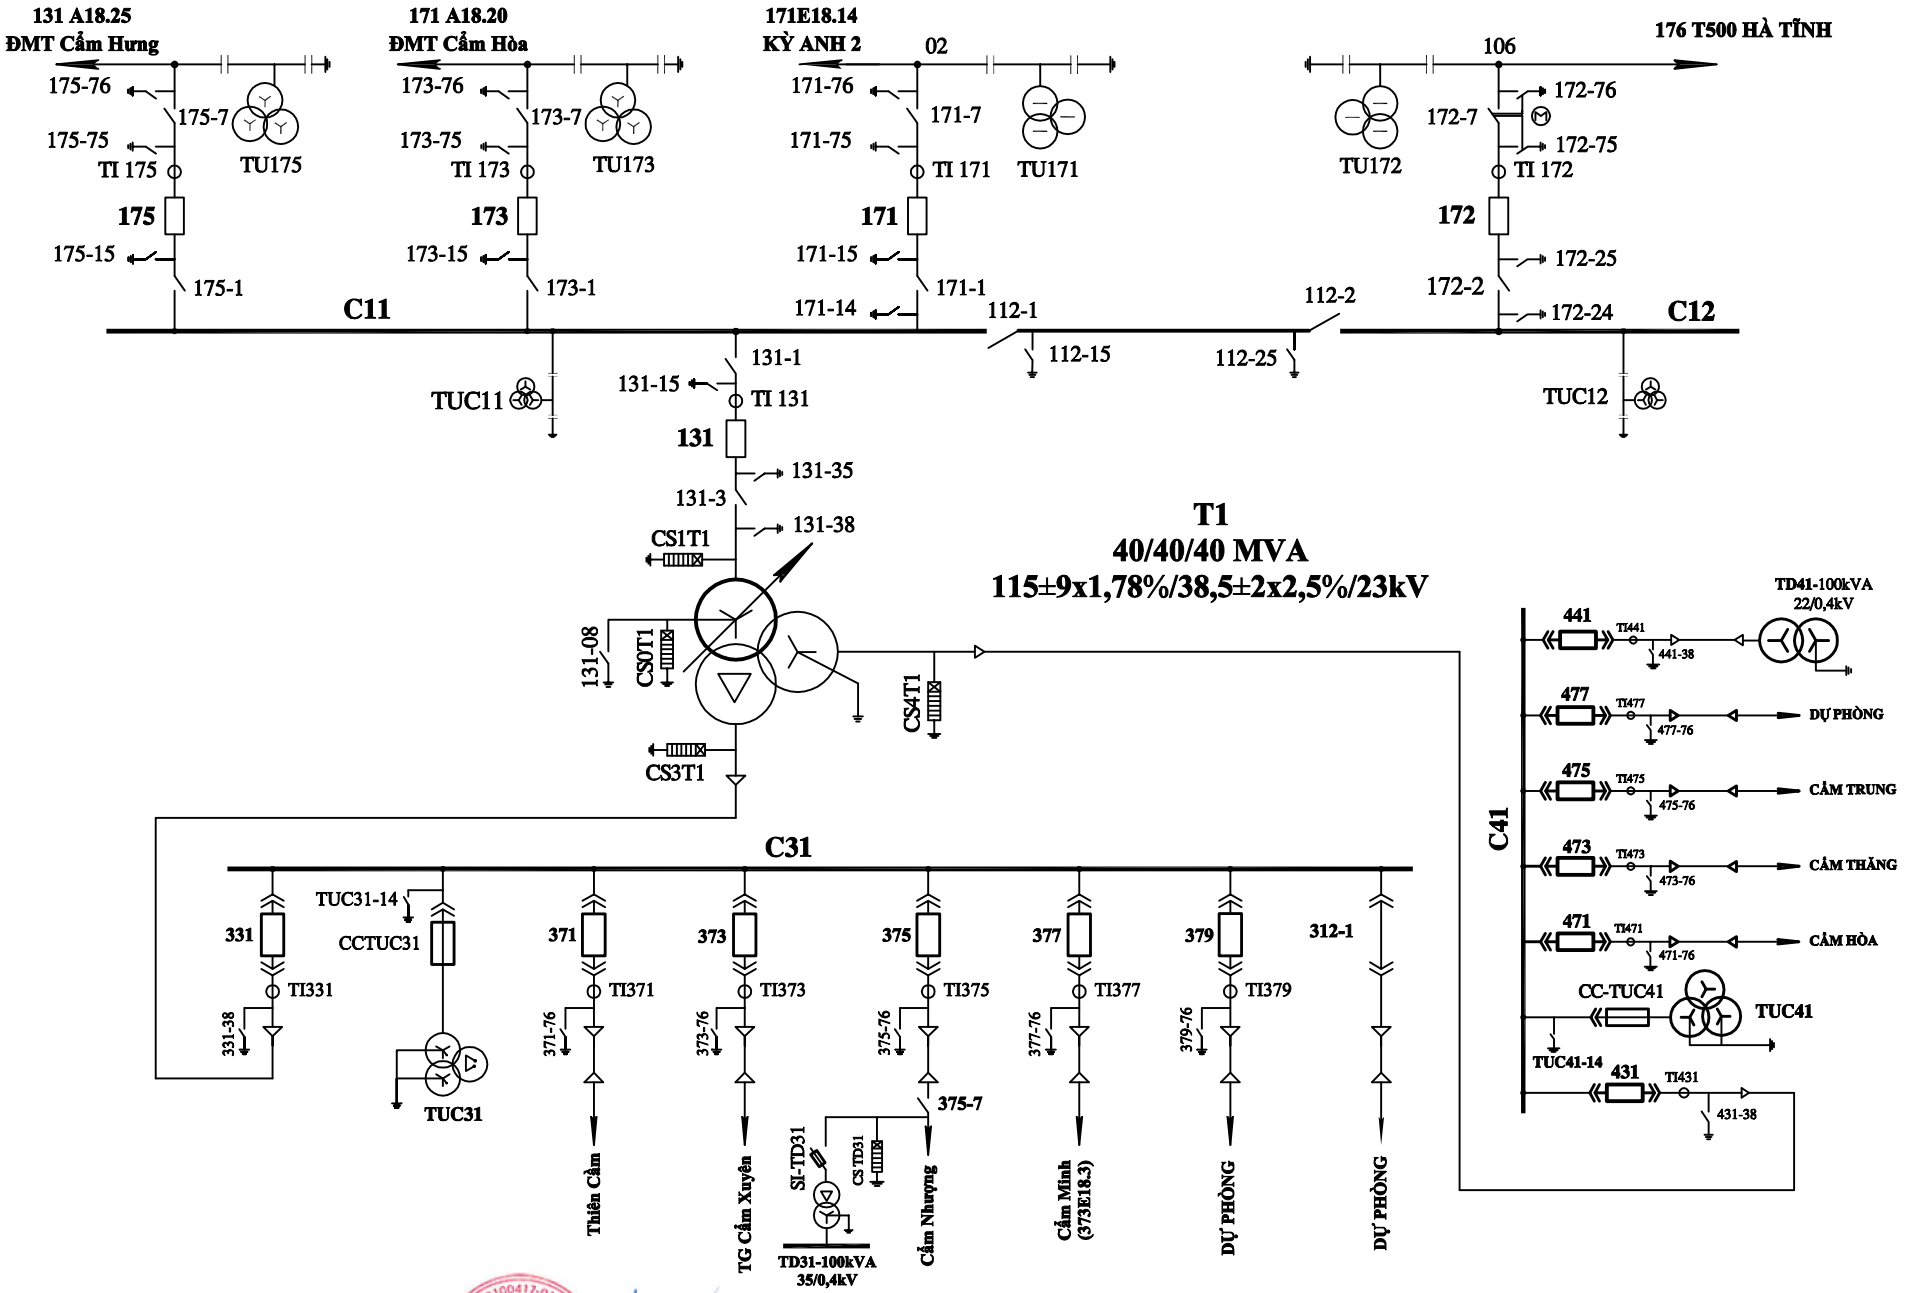

	P.GIÁM ĐỐC	TR. PHÒNG ĐIỀU ĐỘ	NGƯỜI VẼ	
TỔNG CÔNG TY ĐIỆN LỰC MIỀN BẮC CÔNG TY ĐIỆN LỰC HÀ TĨNH	PHẠM VIỆT THẮNG	MAI THANH TÙNG	ĐINH QUỐC NAM	SƠ ĐỒ NHẤT THỨ TRẠM 110 CẨM XUYÊN (E18.9)	SBV: E18.9-01/2025/PCHT-TTĐK Hoàn thành: 02/07/202