
SƠ ĐỒ MỘT SỢI LƯỚI ĐIỆN ĐZ 371 VÀ 375E18.9

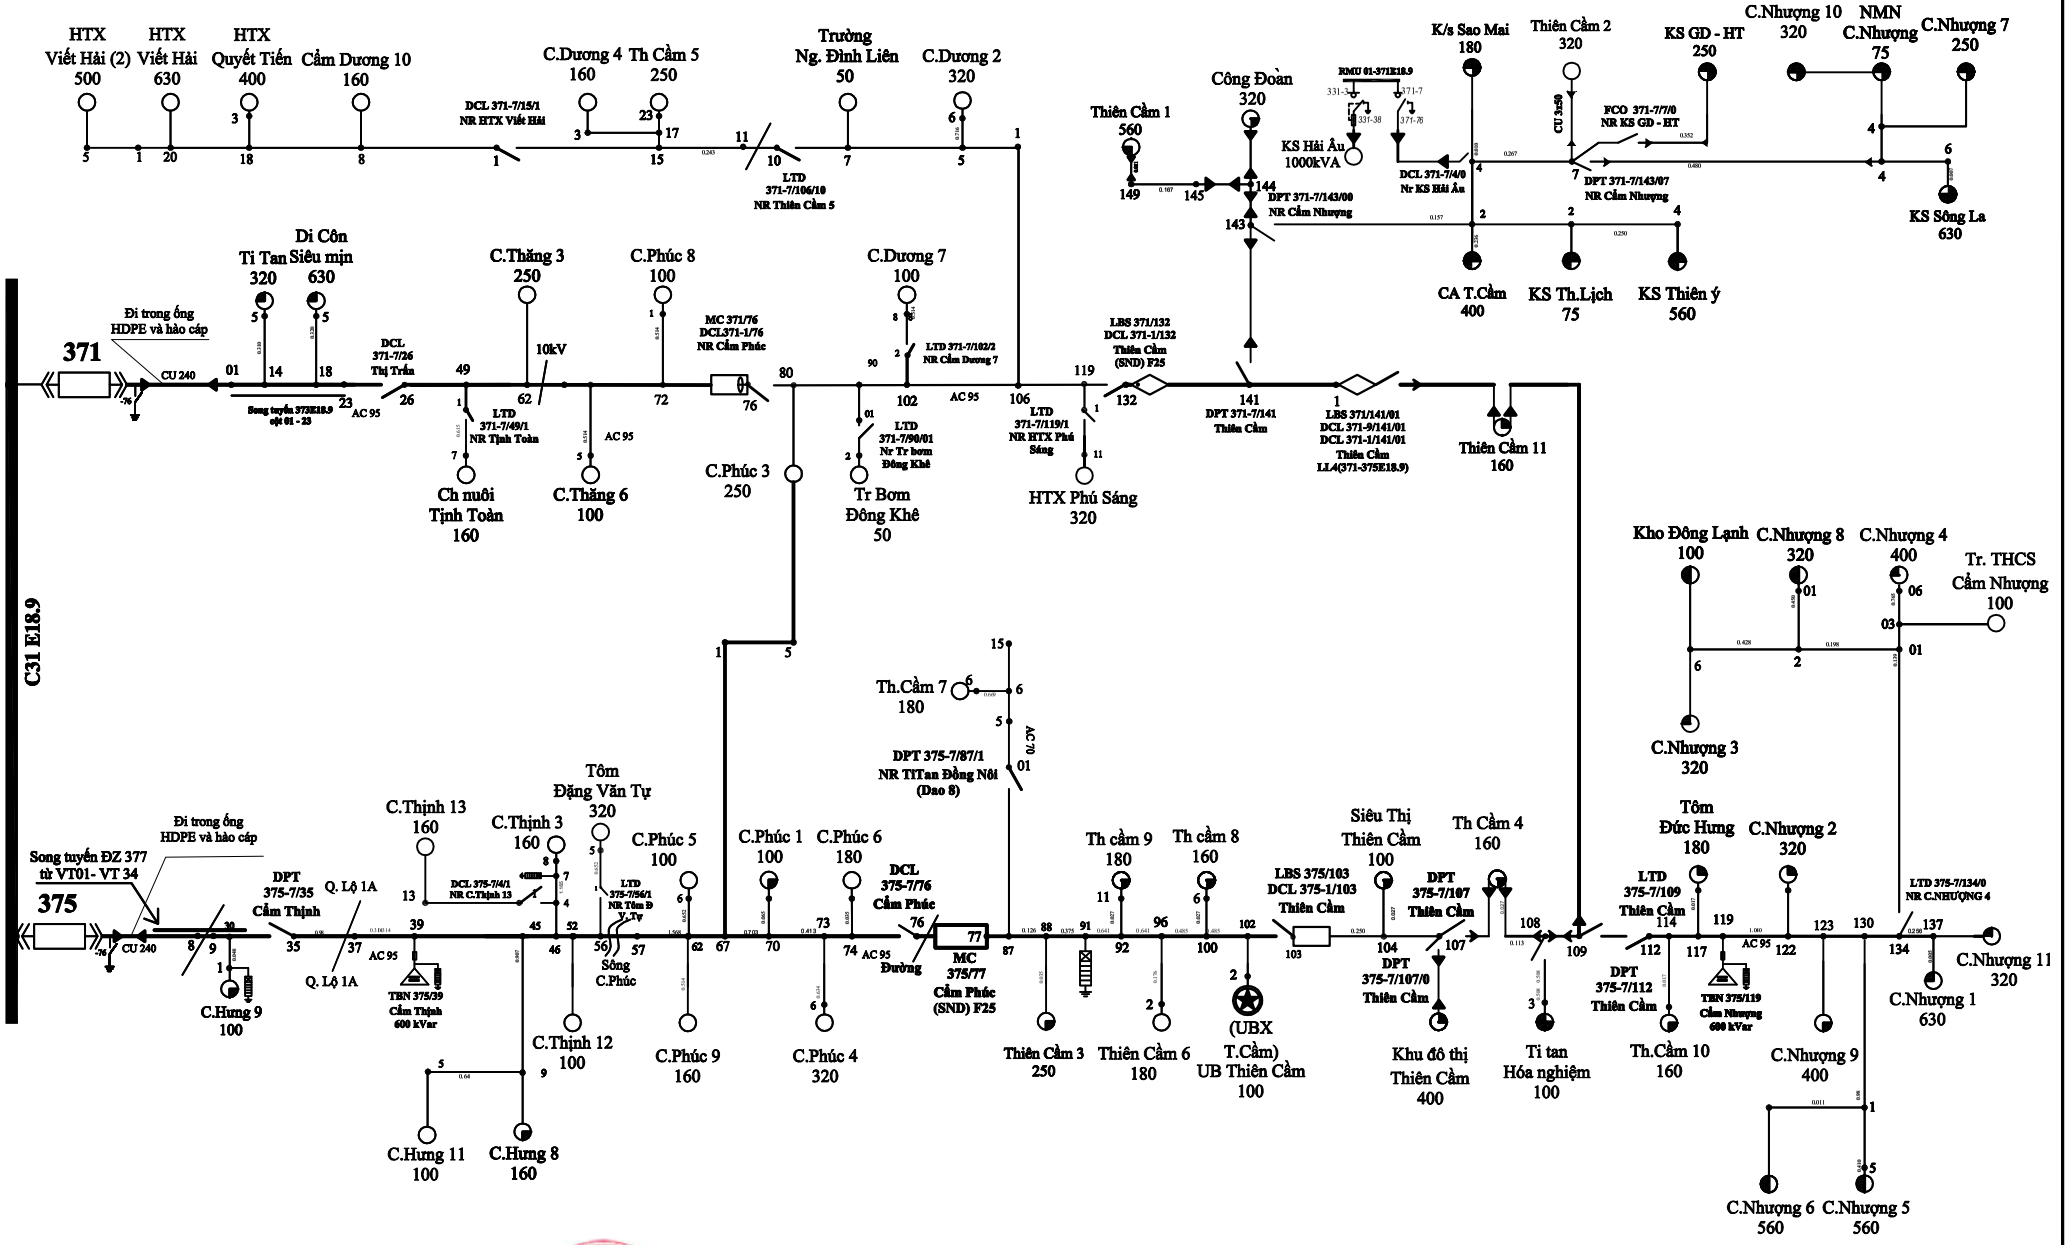

P.GIÁM ĐỐC	TR. PHÒNG ĐIỀU ĐỘ	NGƯỜI VẼ
PHẠM VIỆT THẮNG	MAI THANH TÙNG	ĐINH QUỐC NAM

EVN

TỔNG CÔNG TY ĐIỆN LỰC MIỀN BẮC
CÔNG TY ĐIỆN LỰC HÀ TĨNH

ĐZ 471 E18.9

SƠ ĐỒ MỘT SỢI LƯỚI ĐIỆN CẨM XUYÊN
ĐZ 371, 375E18.9

3

Cẩm Xuyên

Hoàn thành: 02/07/202